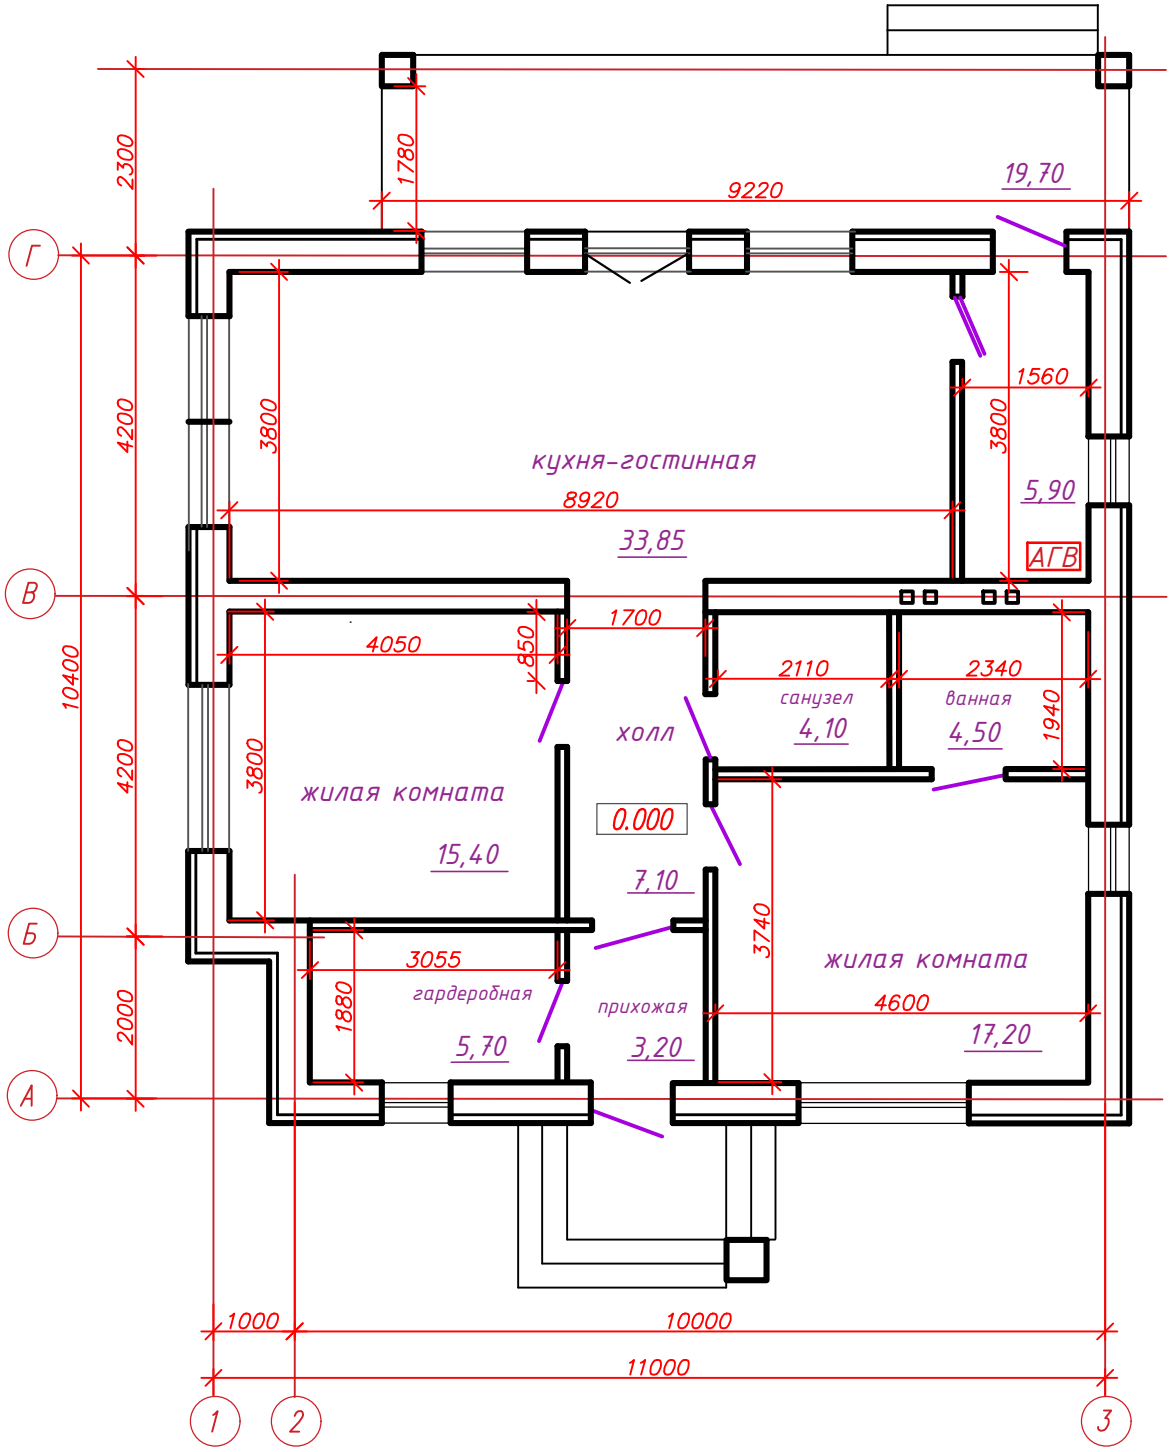
1эт.-3

1кв., 1эт. жд. Общая площадь – 102,27м2 (с террасой)
терраса 19,70х0,3 = 5,31

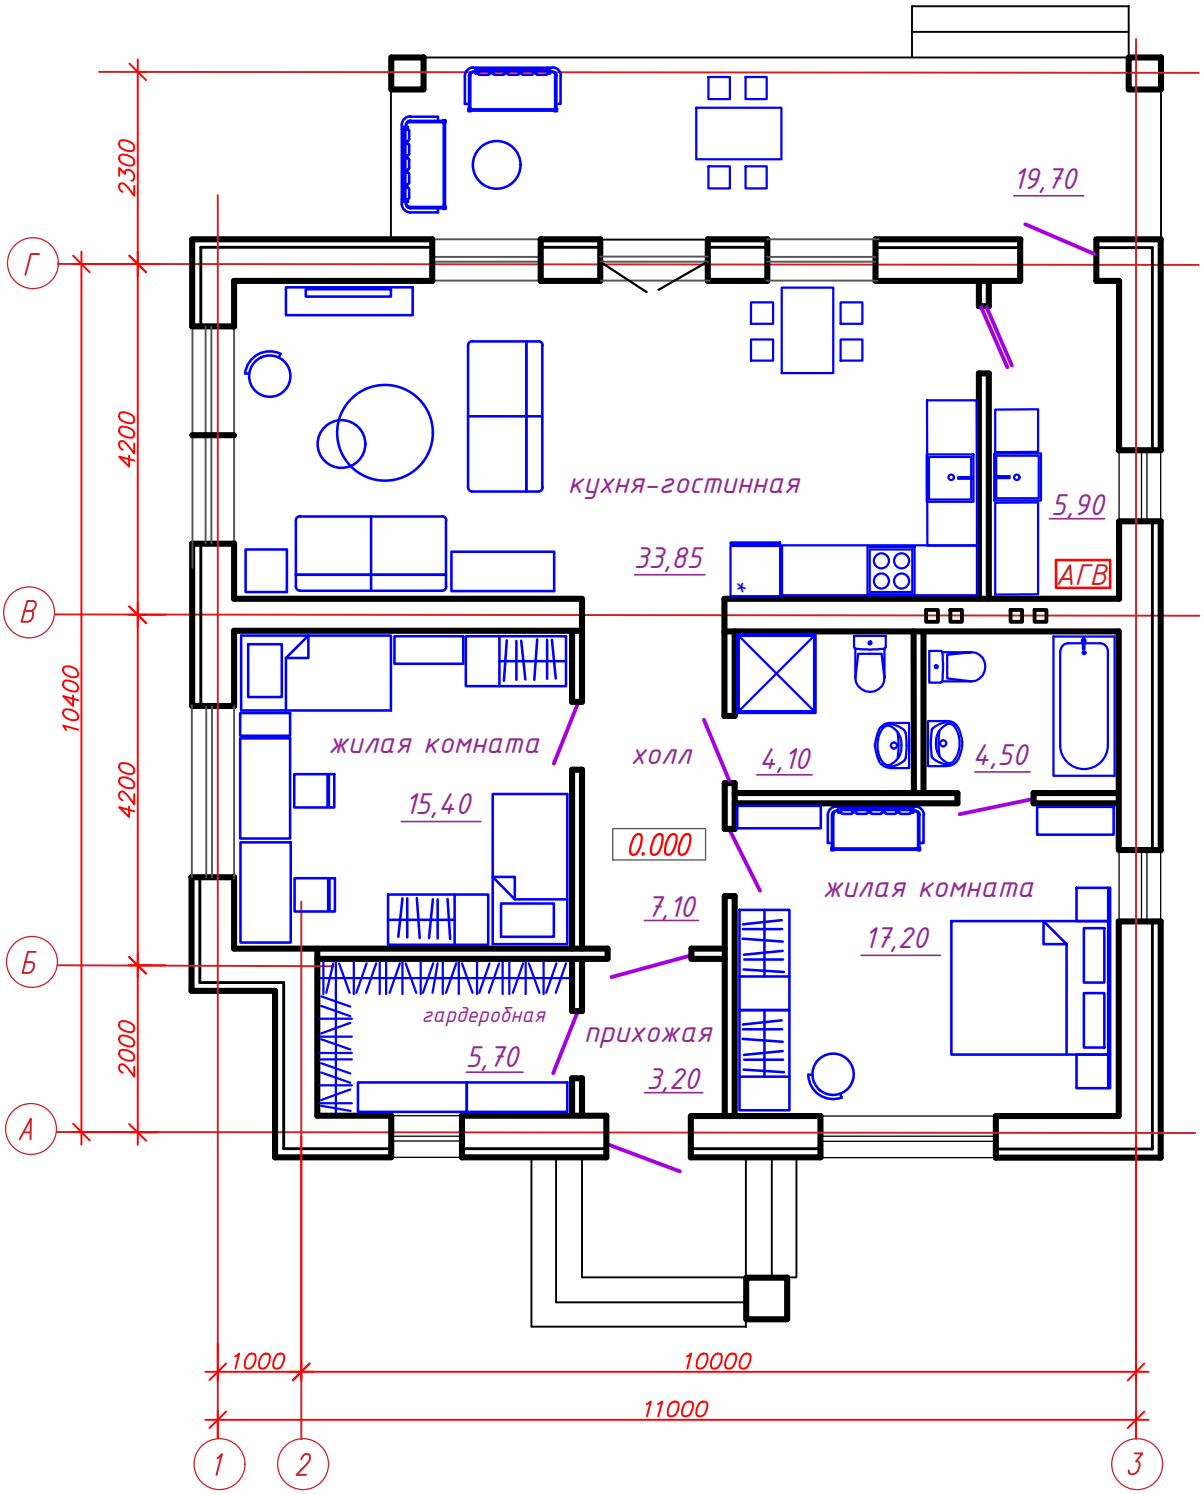
План 1 этажа



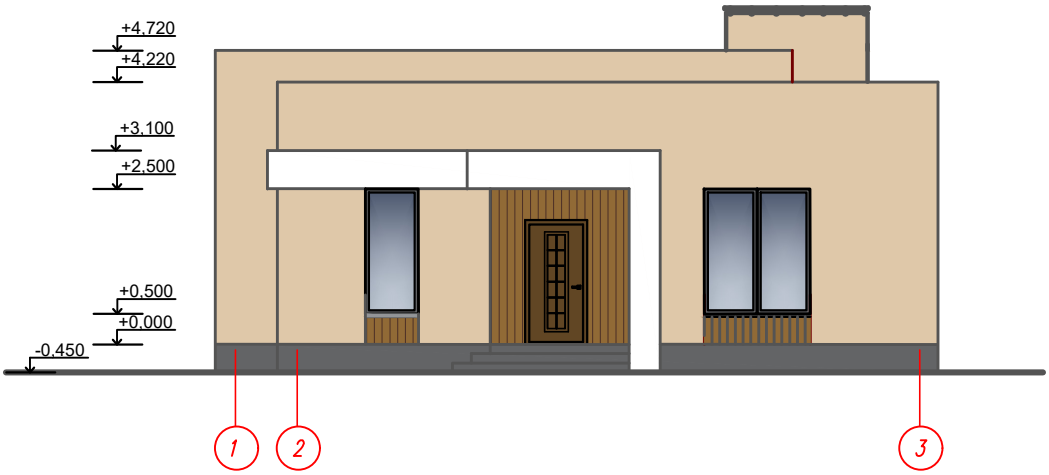
1эт.-3

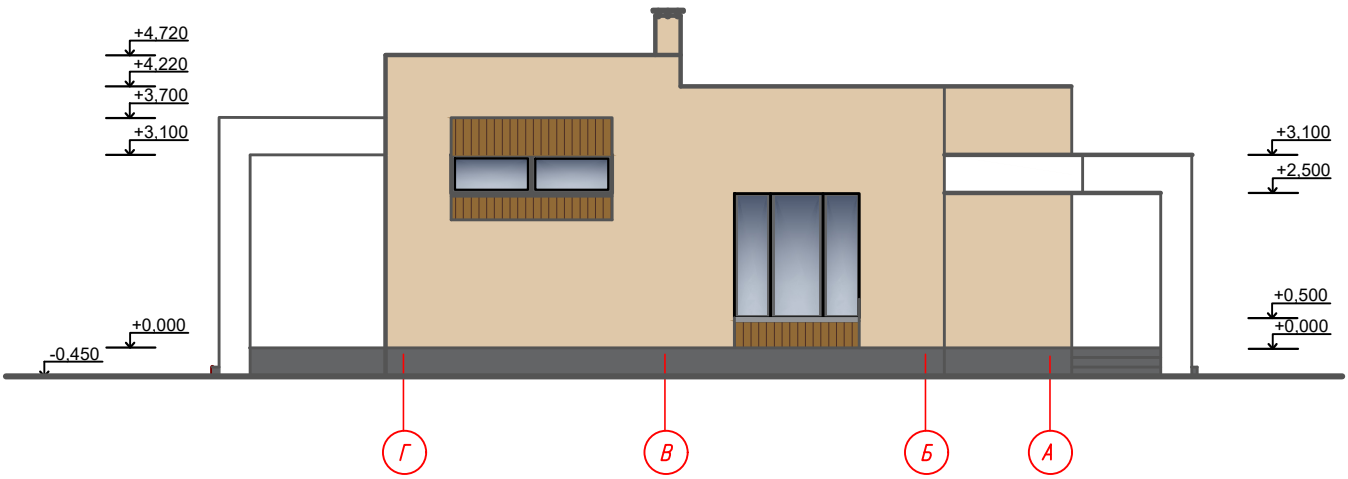
1кв., 1эт. жд. Общая площадь – 102,27м2 (с террасой)
терраса 19,70х0,3 = 5,31

План 1 этажа

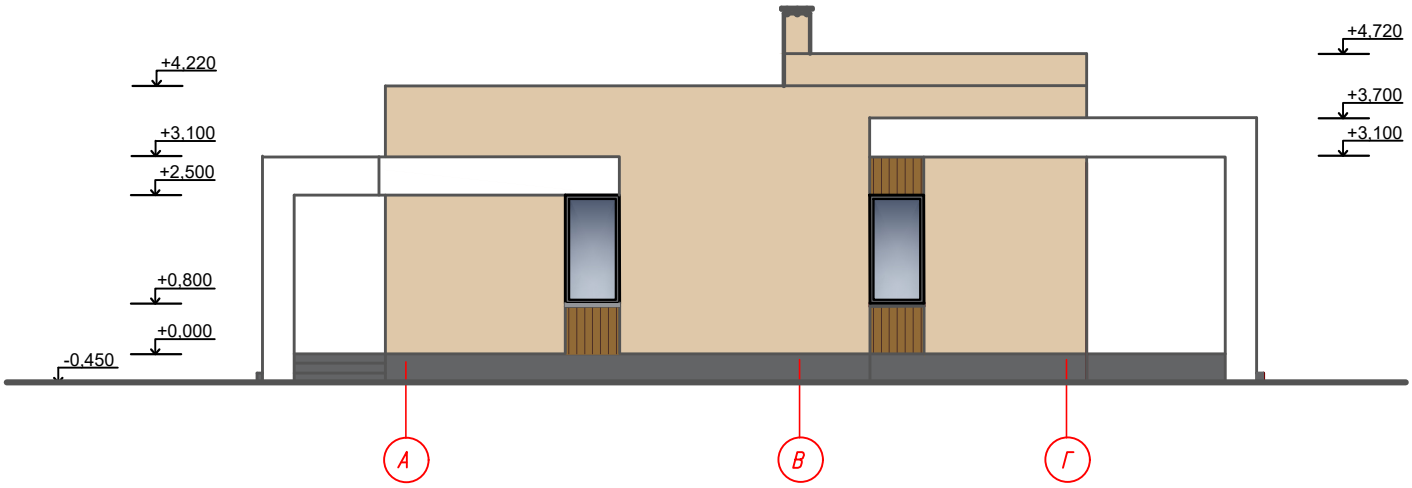


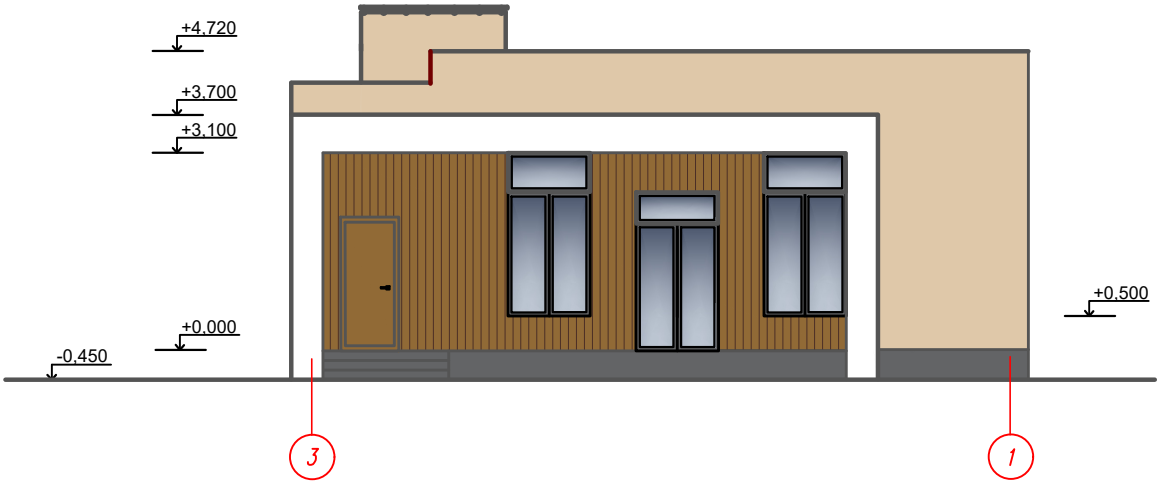
1эт.-3


+4.720
+4.220
+3.100
+2.500
+0.500
+0.000
-0.450
1
2
3


+4.720
+4.220
+3.700
+3.100
+0.000
-0.450
+3.100
+2.500
+0.500
+0.000
Г
В
Б
А

1эт.-3


+4.220
+3.100
+2.500
+0.800
+0.000
-0.450
+4.720
+3.700
+3.100
А
В
Г


+4.720
+3.700
+3.100
+0.000
-0.450
+0.500
3
1